



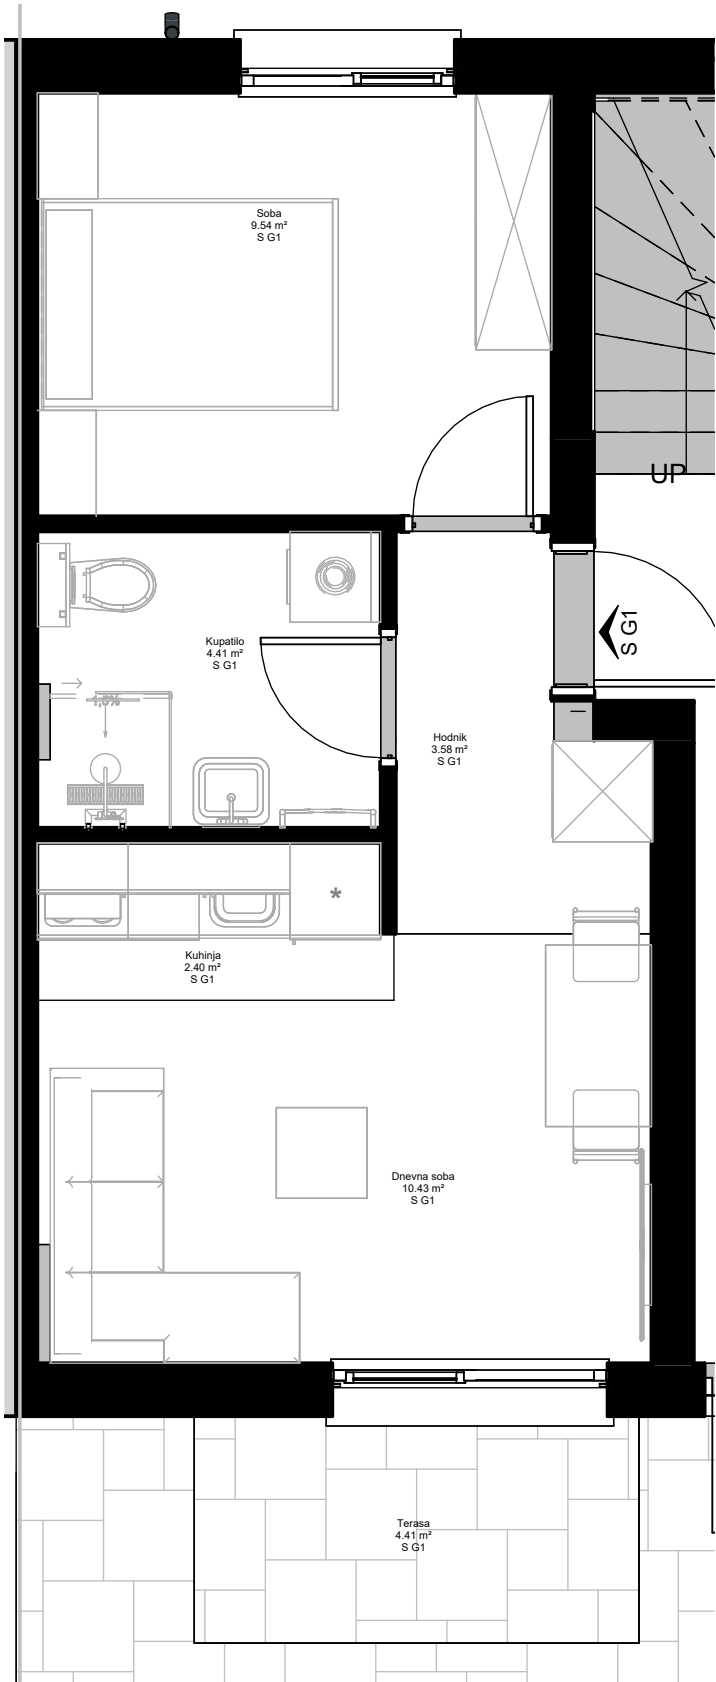

2 C02 - Prizemlje - Stan S G1
1 : 50

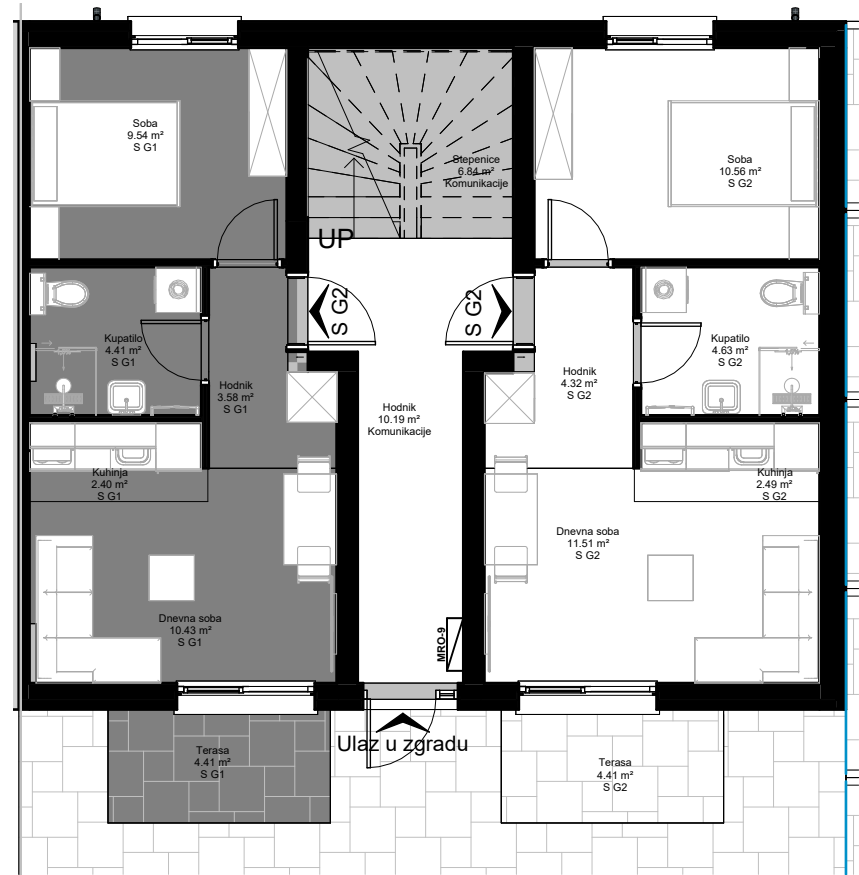


1 C02 - Prizemlje - Položaj stana S G1 na osnovi
1 : 100


A - ONP 03 - Obračun NETO površina Prizemlja					
Broj	Etaza	Etažna jedinica	Naziv	Površina	Grejna površina
29	A 010 - Prizemlje	S G1	Kuhinja	2.40 m²	2.40 m²
30	A 010 - Prizemlje	S G1	Dnevna soba	10.43 m²	10.43 m²
31	A 010 - Prizemlje	S G1	Hodnik	3.58 m²	3.58 m²
32	A 010 - Prizemlje	S G1	Kupatilo	4.41 m²	4.41 m²
33	A 010 - Prizemlje	S G1	Soba	9.54 m²	9.54 m²
40	A 010 - Prizemlje	S G1	Terasa	4.41 m²	0.00 m²
S G1: 6				34.75 m²	30.34 m²
Grand total: 6				34.75 m²	30.34 m²

Stan S G1

Investitor - SUNNY LINE DOO
Autor - ing Radiša Dumonić
Adresa - Novi Sad, Ulica Đakona Avakuma KP 2639/10
Projekat - Porodična stambena zgrada P+1+Pk
Broj projekta - PGD 7037-A01-25.00-002
Datum - Decembar 2025
(deo dvojnog objekta)

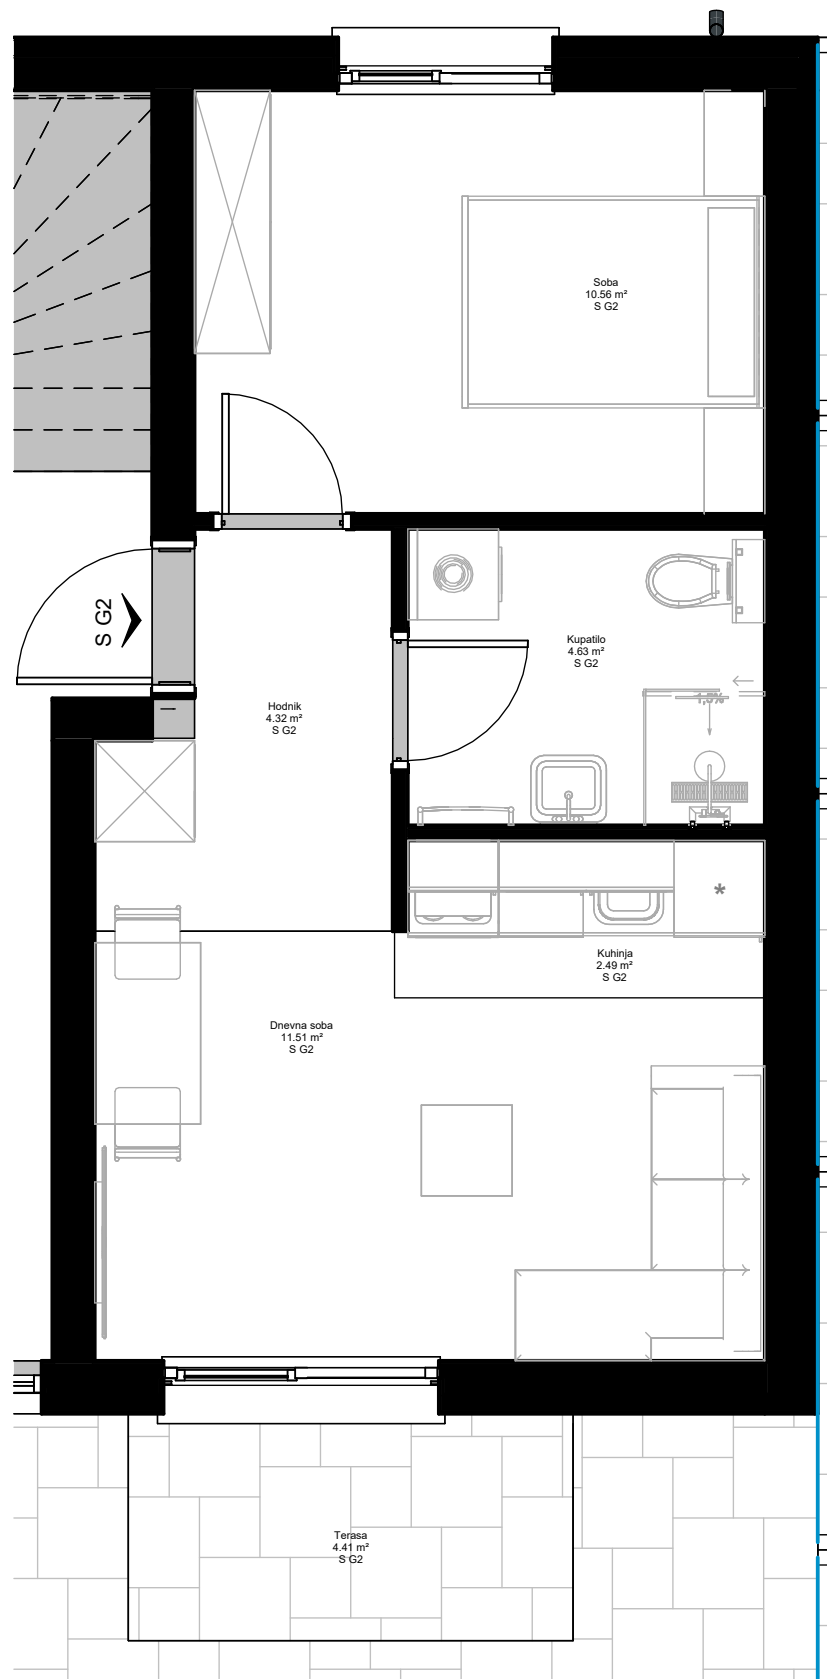

2 C02 - Prizemlje - Stan S G2
1 : 50

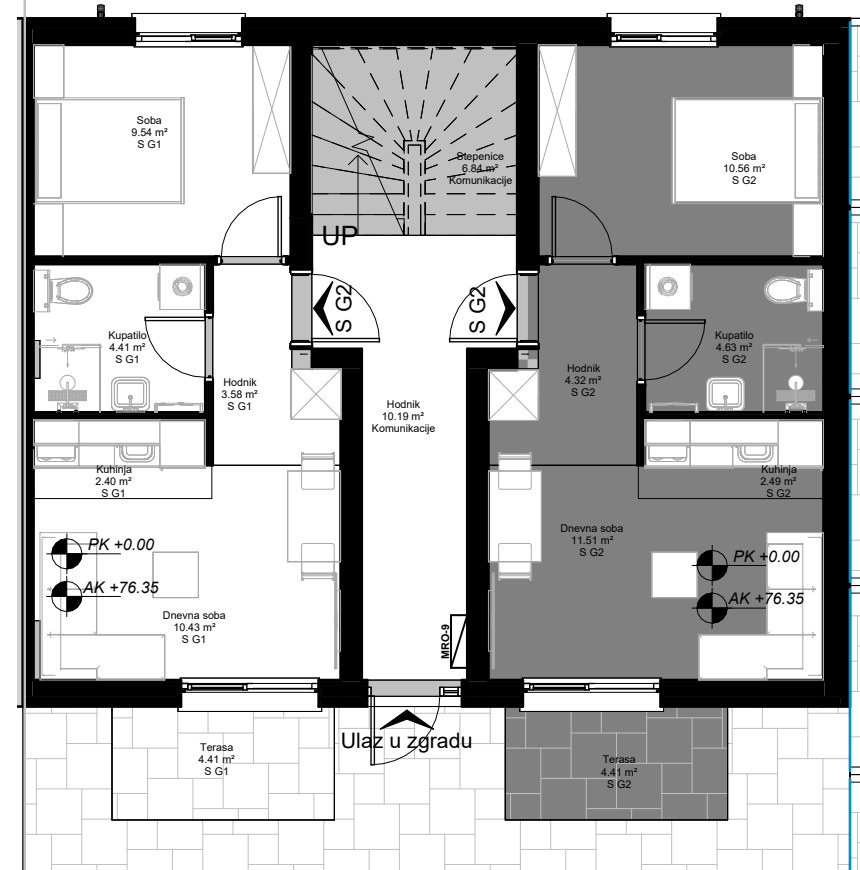


1 C02 - Prizemlje - Položaj stana S G2 na osnovi
1 : 100

A - ONP 03 - Obračun NETO površina Prizemlja Copy 1					
Broj	Etaza	Etažna jedinica	Naziv	Površina	Grejna površina
34	A 010 - Prizemlje	S G2	Soba	10.56 m ²	10.56 m ²
35	A 010 - Prizemlje	S G2	Hodnik	4.32 m ²	4.32 m ²
36	A 010 - Prizemlje	S G2	Kupatilo	4.63 m ²	4.63 m ²
37	A 010 - Prizemlje	S G2	Dnevna soba	11.51 m ²	11.51 m ²
38	A 010 - Prizemlje	S G2	Kuhinja	2.49 m ²	2.49 m ²
39	A 010 - Prizemlje	S G2	Terasa	4.41 m ²	0.00 m ²
S G2: 6				37.93 m ²	33.52 m ²
Grand total: 6				37.93 m ²	33.52 m ²

Stan S G2

Investitor - SUNNY LINE DOO
Autor - ing Radiša Dumonić
Adresa - Novi Sad, Ulica Đakona Avakuma KP 2639/10
Projekat - Porodična stambena zgrada P+1+Pk
Broj projekta - PGD 7037-A01-25.00-002
Datum - Decembar 2025

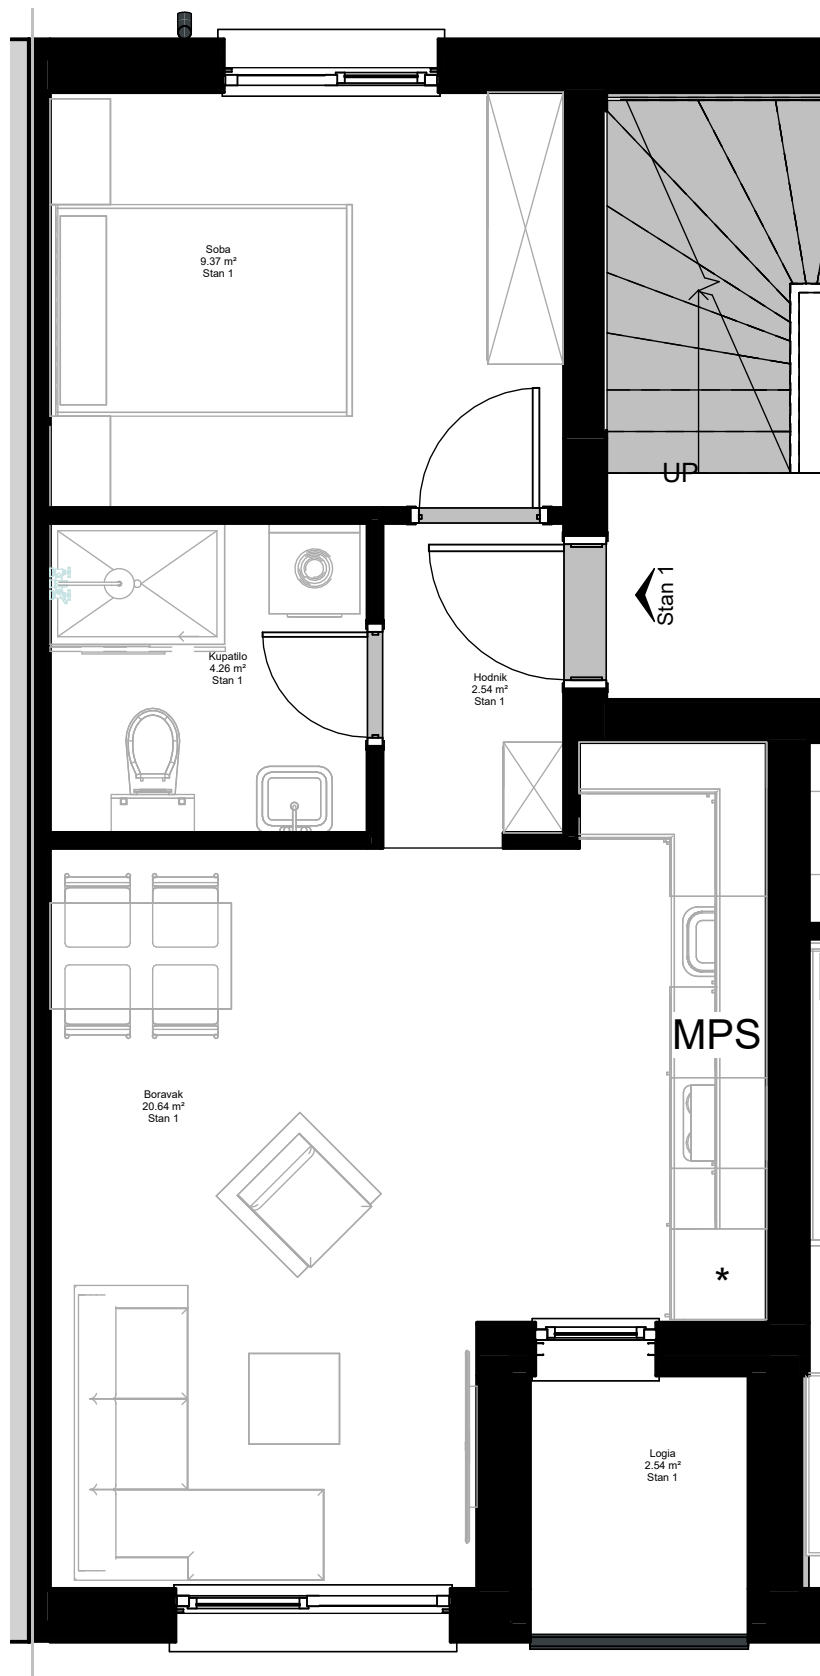

1

C02 - Sprat - Položaj stana 1 na osnovi

1 : 100

A - ONP 04 - Obračun NETO površina stana 3

Broj	Etaza	Etažna jedinica	Naziv	Površina	Red. površina prema SRPS	K	Grejna površina
20	A 030 - Potkrovlje	Stan 3	Boravak	28.04 m ²	27.20 m ²	1	28.04 m ²
21	A 030 - Potkrovlje	Stan 3	Hodnik	6.79 m ²	6.58 m ²	1	6.79 m ²
22	A 030 - Potkrovlje	Stan 3	Soba	10.54 m ²	10.22 m ²	1	10.54 m ²
23	A 030 - Potkrovlje	Stan 3	WC	1.99 m ²	1.93 m ²	1	1.99 m ²
24	A 030 - Potkrovlje	Stan 3	Soba	11.04 m ²	10.71 m ²	1	11.04 m ²
25	A 030 - Potkrovlje	Stan 3	Soba	10.05 m ²	9.74 m ²	1	10.05 m ²
26	A 030 - Potkrovlje	Stan 3	Kupatilo	4.89 m ²	4.74 m ²	1	4.89 m ²
27	A 030 - Potkrovlje	Stan 3	Terasa	32.35 m ²	31.38 m ²	0	0.00 m ²
Stan 3: 8				105.68 m ²	102.51 m ²		73.33 m ²
Grand total: 8				105.68 m ²	102.51 m ²		73.33 m ²

2


C02 - Sprat - Stan 1

1 : 50


Stan 1

(deo dvojnog objekta)

Investitor - SUNNY LINE DOO
Autor - Ing Radiša Dumonić
Adresa - Novi Sad, Ulica Đakona Avakuma KP 2639/10
Projekat - Porodična stambena zgrada P+1+Pk
Broj projekta - PGD 7037-A01-25.00-002
Datum - Decembar 2025


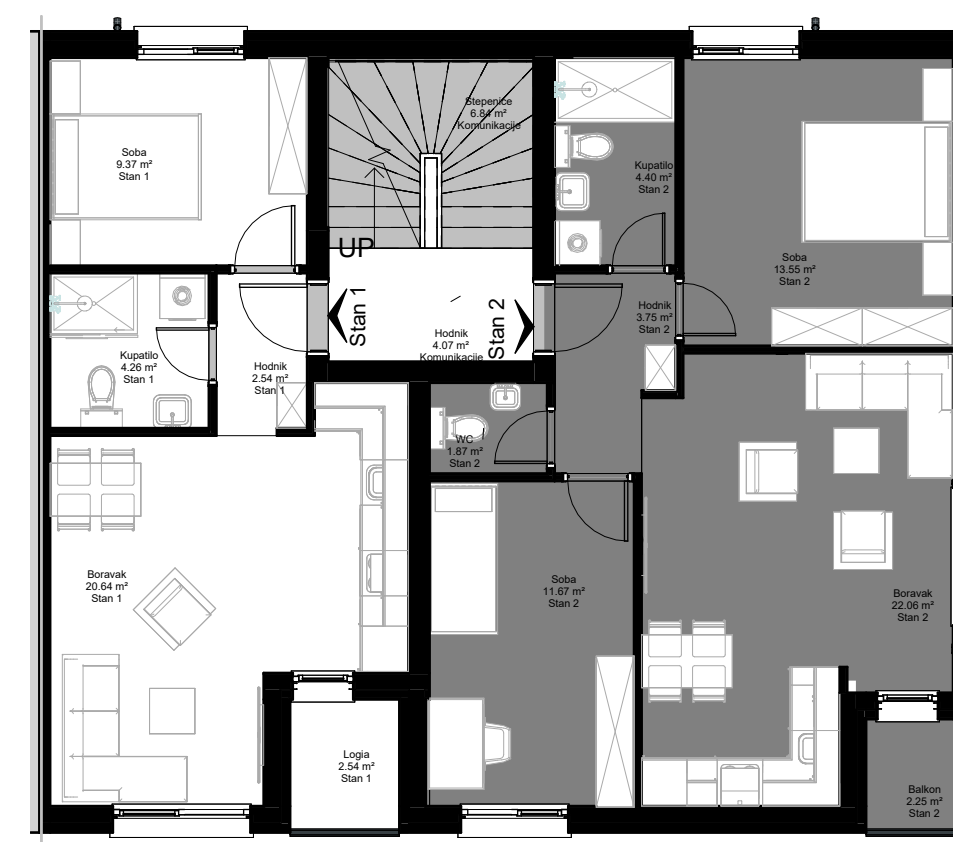


1 C02 - Sprat - Položaj stana 2 na osnovi
1 : 100

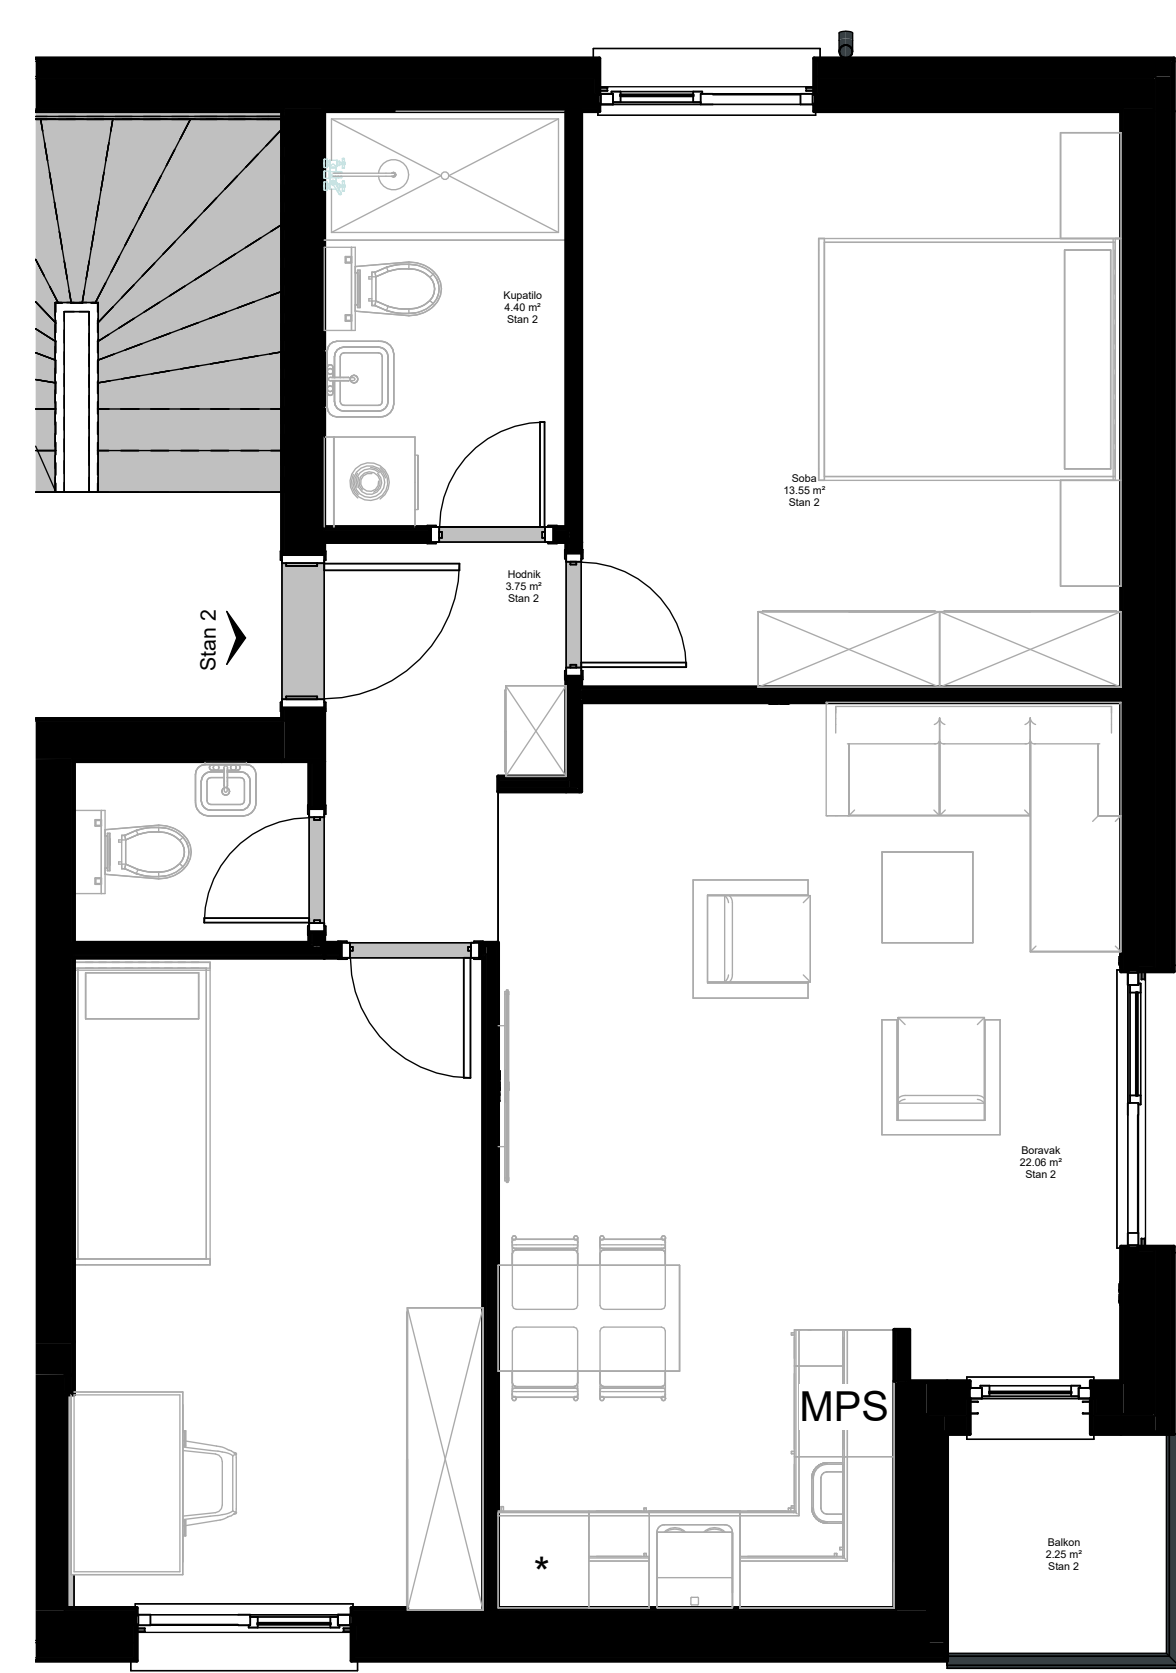

2 C02 - Sprat - Stan 2
1 : 50

A - ONP 04 - Obračun NETO površina stana 2							
Broj	Etaza	Etažna jedinica	Naziv	Površina	Red. površina prema SRPS	K	Grejna površina
12	A 020 - 1 Sprat	Stan 2	Soba	13.55 m ²	13.14 m ²	1	13.55 m ²
13	A 020 - 1 Sprat	Stan 2	WC	1.87 m ²	1.81 m ²	1	1.87 m ²
14	A 020 - 1 Sprat	Stan 2	Hodnik	3.75 m ²	3.63 m ²	1	3.75 m ²
15	A 020 - 1 Sprat	Stan 2	Boravak	22.06 m ²	21.39 m ²	1	22.06 m ²
16	A 020 - 1 Sprat	Stan 2	Kupatilo	4.40 m ²	4.27 m ²	1	4.40 m ²
17	A 020 - 1 Sprat	Stan 2	Soba	11.67 m ²	11.32 m ²	1	11.67 m ²
18	A 020 - 1 Sprat	Stan 2	Balkon	2.25 m ²	2.18 m ²	0	0.00 m ²
Stan 2: 7				59.53 m ²	57.75 m ²		57.28 m ²
Grand total: 7				59.53 m ²	57.75 m ²		57.28 m ²

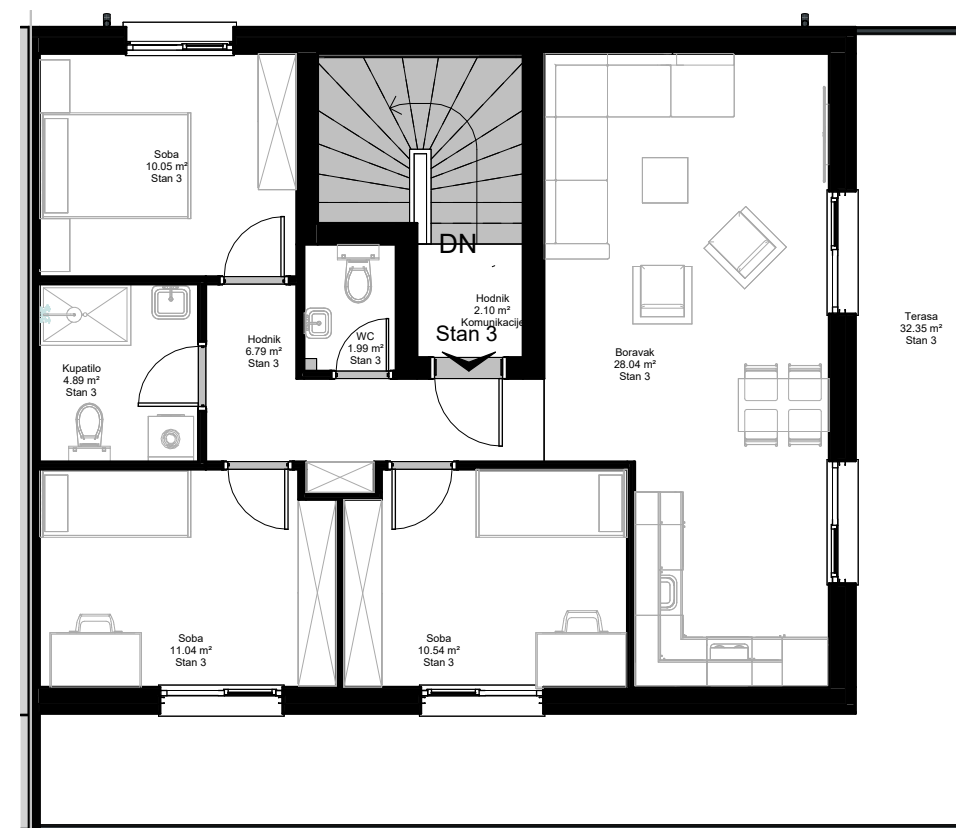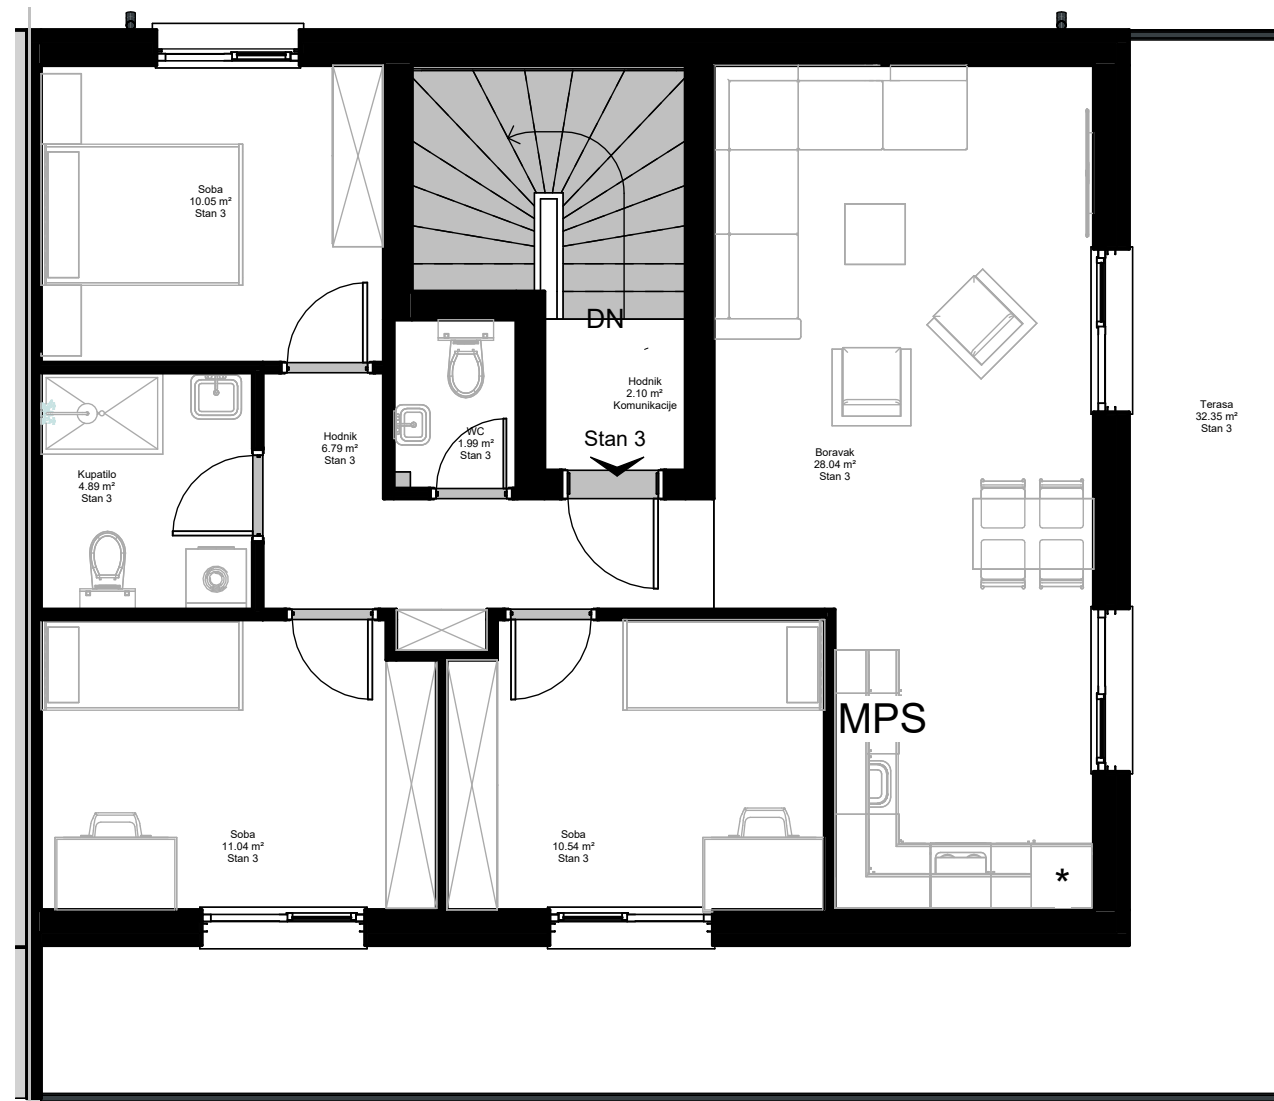

1 C02 - Potkrovlje - Položaj stana 3 na osnovi
1 : 100

2 C02 - Potkrovlje - Stan 3
1 : 75

A - ONP 04 - Obračun NETO površina stana 3							
Broj	Etaza	Etažna jedinica	Naziv	Površina	Red. površina prema SRPS	K	Grejna površina
20	A 030 - Potkrovlje	Stan 3	Boravak	28.04 m ²	27.20 m ²	1	28.04 m ²
21	A 030 - Potkrovlje	Stan 3	Hodnik	6.79 m ²	6.58 m ²	1	6.79 m ²
22	A 030 - Potkrovlje	Stan 3	Soba	10.54 m ²	10.22 m ²	1	10.54 m ²
23	A 030 - Potkrovlje	Stan 3	WC	1.99 m ²	1.93 m ²	1	1.99 m ²
24	A 030 - Potkrovlje	Stan 3	Soba	11.04 m ²	10.71 m ²	1	11.04 m ²
25	A 030 - Potkrovlje	Stan 3	Soba	10.05 m ²	9.74 m ²	1	10.05 m ²
26	A 030 - Potkrovlje	Stan 3	Kupatilo	4.89 m ²	4.74 m ²	1	4.89 m ²
27	A 030 - Potkrovlje	Stan 3	Terasa	32.35 m ²	31.38 m ²	0	0.00 m ²
Stan 3: 8				105.68 m ²	102.51 m ²		73.33 m ²
Grand total: 8				105.68 m ²	102.51 m ²		73.33 m ²

Stan 3

(deo dvojnog objekta)

Investitor - SUNNY LINE DOO
Autor - Ing Radiša Dumonić
Adresa - Novi Sad, Ulica Đakona Avakuma KP 2639/10
Projekat - Porodična stambena zgrada P+1+Pk
Broj projekta - PGD 7037-A01-25.00-002
Datum - Decembar 2025