




2 C02 - Prizemlje - Stan S G1
1 : 50

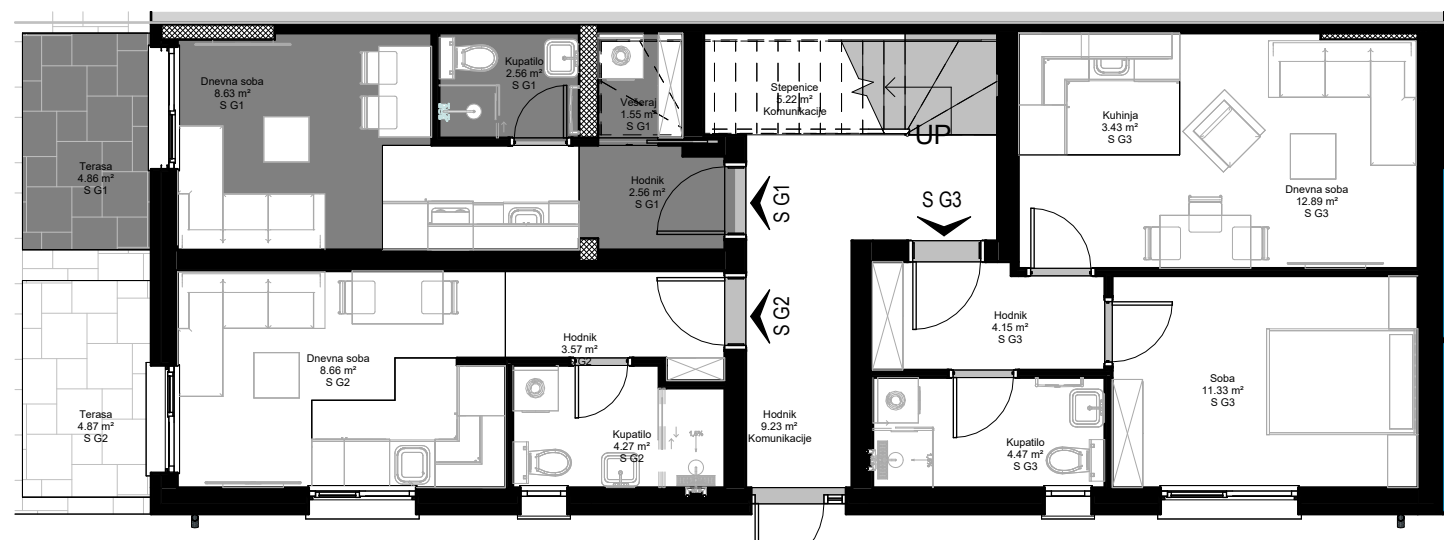


1 C02 - Prizemlje - Položaj
stana S G1 na osnovi
1 : 100


A - ONP 03 - Obračun NETO površina stana S G1					
Broj	Etaza	Etažna jedinica	Naziv	Površina	Grejna površina
35	A 010 - Prizemlje	S G1	Hodnik	2.56 m ²	2.56 m ²
38	A 010 - Prizemlje	S G1	Dnevna soba	8.63 m ²	8.63 m ²
39	A 010 - Prizemlje	S G1	Kupatilo	2.56 m ²	2.56 m ²
40	A 010 - Prizemlje	S G1	Vešeraj	1.55 m ²	1.55 m ²
41	A 010 - Prizemlje	S G1	Terasa	4.86 m ²	0.00 m ²
S G1: 5				20.16 m ²	15.30 m ²
Grand total: 5				20.16 m ²	15.30 m ²

Stan G S1

Investitor - SUNNY LINE DOO
Autor - ing Radiša Dumonić
Adresa - Novi Sad, Ulica Nova 28 KP 2639/9 KO Novi Sad III
Projekat - Porodična stambena zgrada P+1+Pk
Broj projekta - PGD 7037-A01-25.00-003
Datum - Decembar 2025
(deo dvojnog objekta)

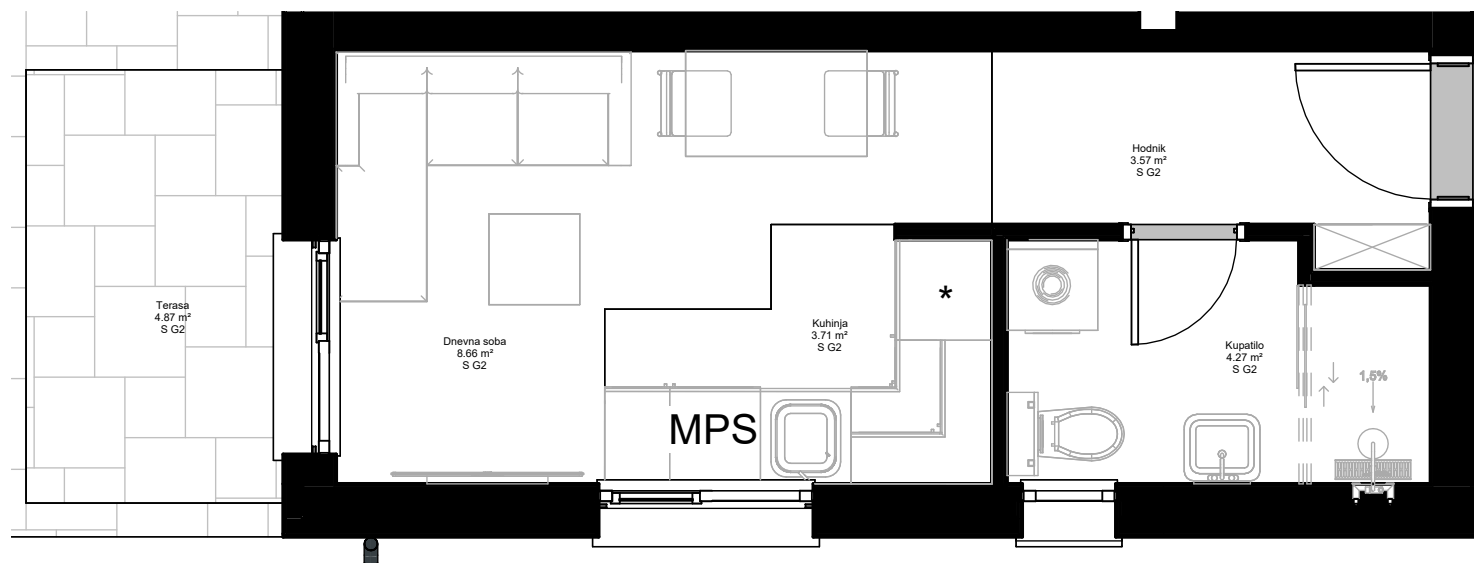

2 C02 - Prizemlje - Stan S G2
1 : 50

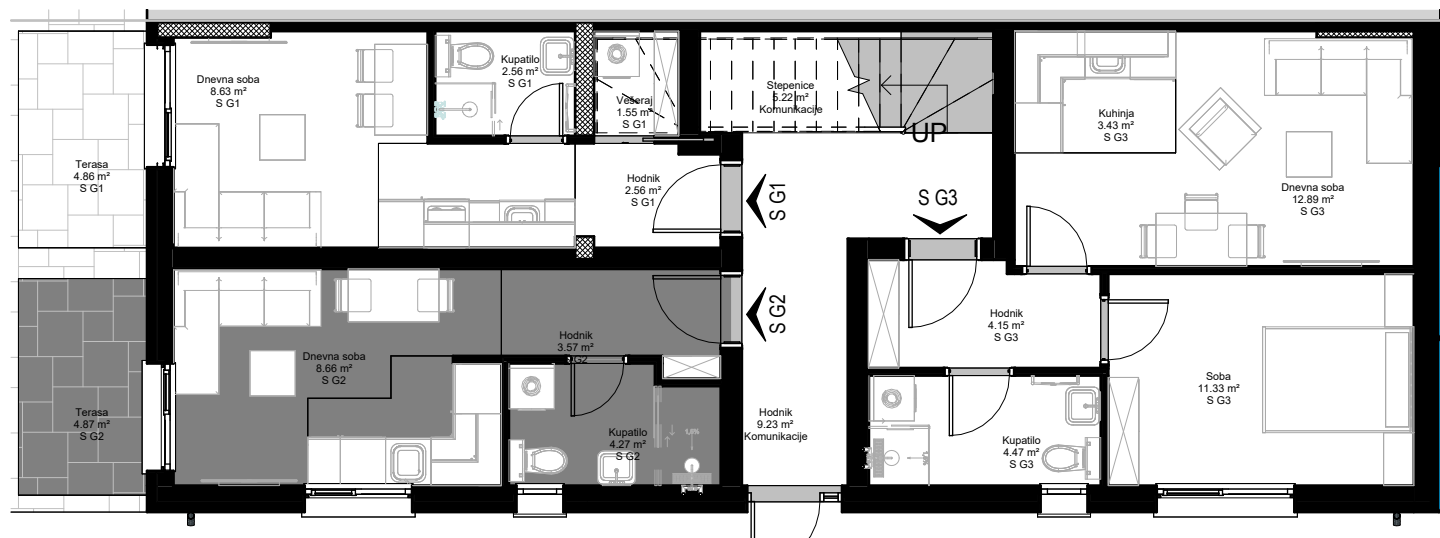

1 C02 - Prizemlje - Položaj
stana S G2 na osnovi
1 : 100

A - ONP 03 - Obračun NETO površina stana S G2					
Broj	Etaza	Etažna jedinica	Naziv	Površina	Grejna površina
42	A 010 - Prizemlje	S G2	Terasa	4.87 m²	0.00 m²
43	A 010 - Prizemlje	S G2	Hodnik	3.57 m²	3.57 m²
44	A 010 - Prizemlje	S G2	Dnevna soba	8.66 m²	8.66 m²
46	A 010 - Prizemlje	S G2	Kupatilo	4.27 m²	4.27 m²
53	A 010 - Prizemlje	S G2	Kuhinja	3.71 m²	3.71 m²
S G2: 5				25.08 m²	20.21 m²
Grand total: 5				25.08 m²	20.21 m²

Stan G S2

Investitor - SUNNY LINE DOO
Autor - ing Radiša Dumonić
Adresa - Novi Sad, Ulica Nova 28 KP 2639/9 KO Novi Sad III
Projekat - Porodična stambena zgrada P+1+Pk
Broj projekta - PGD 7037-A01-25.00-003
Datum - Decembar 2025
(deo dvojnog objekta)



2 C02 - Prizemlje - Stan S G3
1 : 50



1 C02 - Prizemlje - Položaj
stana S G3 na osnovi
1 : 100

A - ONP 03 - Obračun NETO površina stana S G3					
Broj	Etaza	Etažna jedinica	Naziv	Površina	Grejna površina
47	A 010 - Prizemlje	S G3	Hodnik	4.15 m ²	4.15 m ²
48	A 010 - Prizemlje	S G3	Kupatilo	4.47 m ²	4.47 m ²
49	A 010 - Prizemlje	S G3	Soba	11.33 m ²	11.33 m ²
50	A 010 - Prizemlje	S G3	Kuhinja	3.43 m ²	3.43 m ²
51	A 010 - Prizemlje	S G3	Dnevna soba	12.89 m ²	12.89 m ²
52	A 010 - Prizemlje	S G3	Kuhinja	3.59 m ²	3.59 m ²
S G3: 6				39.86 m ²	39.86 m ²
Grand total: 6				39.86 m ²	39.86 m ²

Stan G S3

Investitor - SUNNY LINE DOO
Autor - Ing Radiša Dumonić
Adresa - Novi Sad, Ulica Nova 28 KP 2639/9 KO Novi Sad III
Projekat - Porođična stambena zgrada P+1+Pk
Broj projekta - PGD 7037-A01-25.00-003
Datum - Decembar 2025



2 C02 - Sprat - Stan 1
1 : 50




1 C02 - Sprat - Položaj stana
1 na osnovi
1 : 100

A - ONP 04 - Obračun NETO površina stana 1					
Broj	Etaza	Etažna jedinica	Naziv	Površina	Grejna površina
8	A 020 - 1 Sprat	Stan 1	Logia	2.96 m ²	0.00 m ²
9	A 020 - 1 Sprat	Stan 1	Soba	8.83 m ²	8.83 m ²
10	A 020 - 1 Sprat	Stan 1	Dnevna soba	15.50 m ²	15.50 m ²
11	A 020 - 1 Sprat	Stan 1	Hodnik	4.79 m ²	4.79 m ²
12	A 020 - 1 Sprat	Stan 1	Kupatilo	4.34 m ²	4.34 m ²
13	A 020 - 1 Sprat	Stan 1	Soba	7.93 m ²	7.93 m ²
33	A 020 - 1 Sprat	Stan 1	Kuhinja	2.91 m ²	2.91 m ²
Stan 1: 7				47.25 m ²	44.29 m ²
Grand total: 7				47.25 m ²	44.29 m ²



2 C02 - Sprat - Stan 2
1 : 50

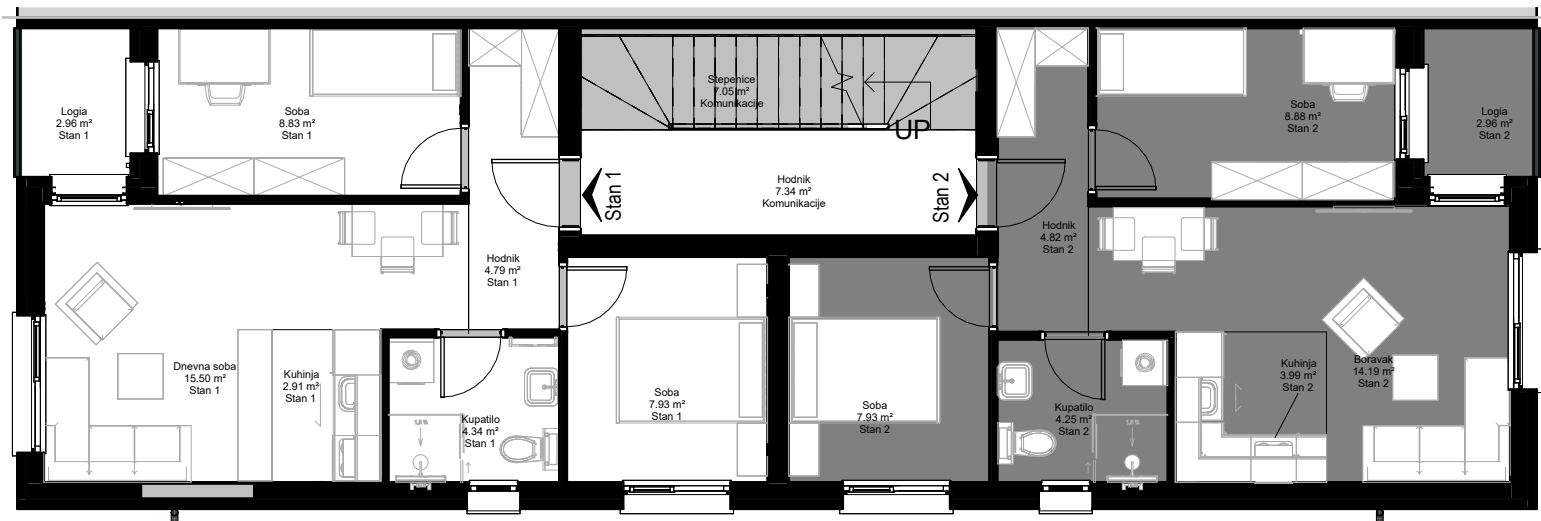

1 C02 - Sprat - Položaj stana
2 na osnovi
1 : 100


A - ONP 04 - Obračun NETO površina stana 2					
Broj	Etaza	Etažna jedinica	Naziv	Površina	Grejna površina
14	A 020 - 1 Sprat	Stan 2	Soba	7.93 m ²	7.93 m ²
15	A 020 - 1 Sprat	Stan 2	Hodnik	4.82 m ²	4.82 m ²
16	A 020 - 1 Sprat	Stan 2	Kupatilo	4.25 m ²	4.25 m ²
17	A 020 - 1 Sprat	Stan 2	Soba	8.88 m ²	8.88 m ²
18	A 020 - 1 Sprat	Stan 2	Boravak	14.19 m ²	14.19 m ²
19	A 020 - 1 Sprat	Stan 2	Logia	2.96 m ²	0.00 m ²
34	A 020 - 1 Sprat	Stan 2	Kuhinja	3.99 m ²	3.99 m ²
Stan 2: 7				47.02 m ²	44.06 m ²
Grand total: 7				47.02 m ²	44.06 m ²

Stan 2

Investitor - SUNNY LINE DOO
Autor - Ing Radiša Dumonić
Adresa - Novi Sad, Ulica Nova 28 KP 2639/9 KO Novi Sad III
Projekat - Porodična stambena zgrada P+1+Pk
Broj projekta - PGD 7037-A01-25.00-003
Datum - Decembar 2025



2 C02 - Potkrovlje - Stan 3
1 : 75

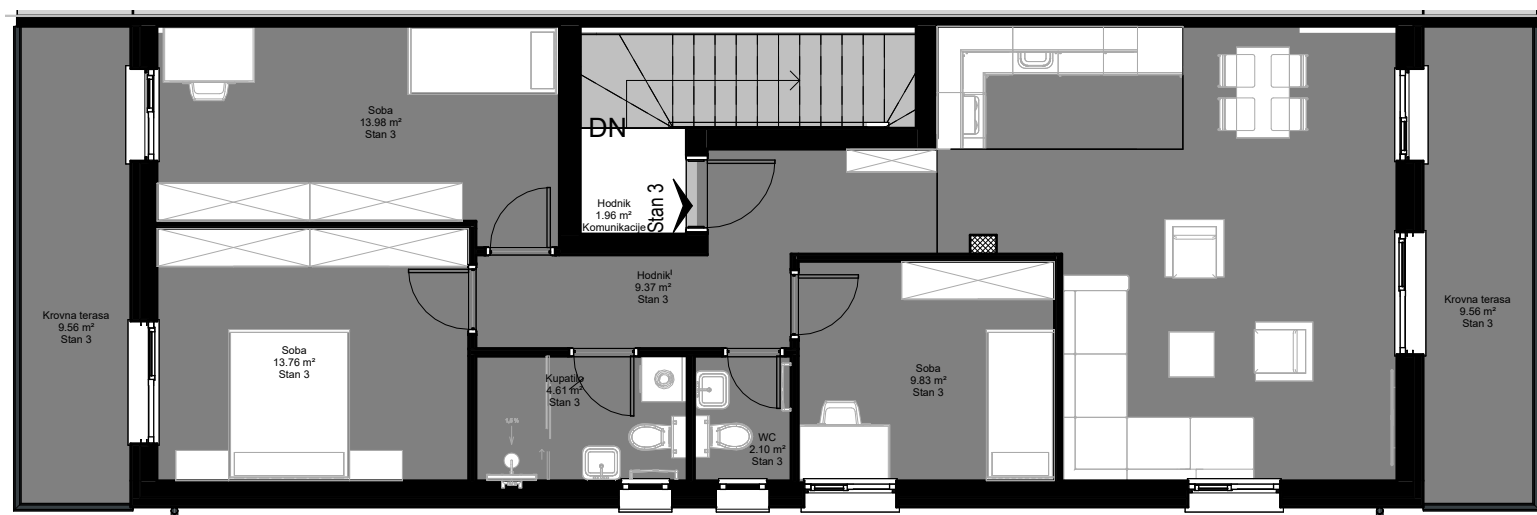

1 C02 - Potkrovlje - Položaj
stana 3 na osnovi
1 : 100

A - ONP 05 - Obračun NETO površina stana 3					
Broj	Etaza	Etažna jedinica	Naziv	Površina	Grejna površina
21	A 030 - Potkrovlje	Stan 3	Soba	13.98 m ²	13.98 m ²
22	A 030 - Potkrovlje	Stan 3	Soba	13.76 m ²	13.76 m ²
23	A 030 - Potkrovlje	Stan 3	Hodnik	9.37 m ²	9.37 m ²
24	A 030 - Potkrovlje	Stan 3	Kupatilo	4.61 m ²	4.61 m ²
25	A 030 - Potkrovlje	Stan 3	WC	2.10 m ²	2.10 m ²
26	A 030 - Potkrovlje	Stan 3	Soba	9.83 m ²	9.83 m ²
30	A 030 - Potkrovlje	Stan 3	Krovnna terasa	9.56 m ²	0.00 m ²
32	A 030 - Potkrovlje	Stan 3	Krovnna terasa	9.56 m ²	0.00 m ²
54	A 030 - Potkrovlje	Stan 3	Dnevna soba	26.14 m ²	26.14 m ²
55	A 030 - Potkrovlje	Stan 3	Kuhinja	5.26 m ²	5.26 m ²
Stan 3: 10				104.17 m ²	85.05 m ²
Grand total: 10				104.17 m ²	85.05 m ²